


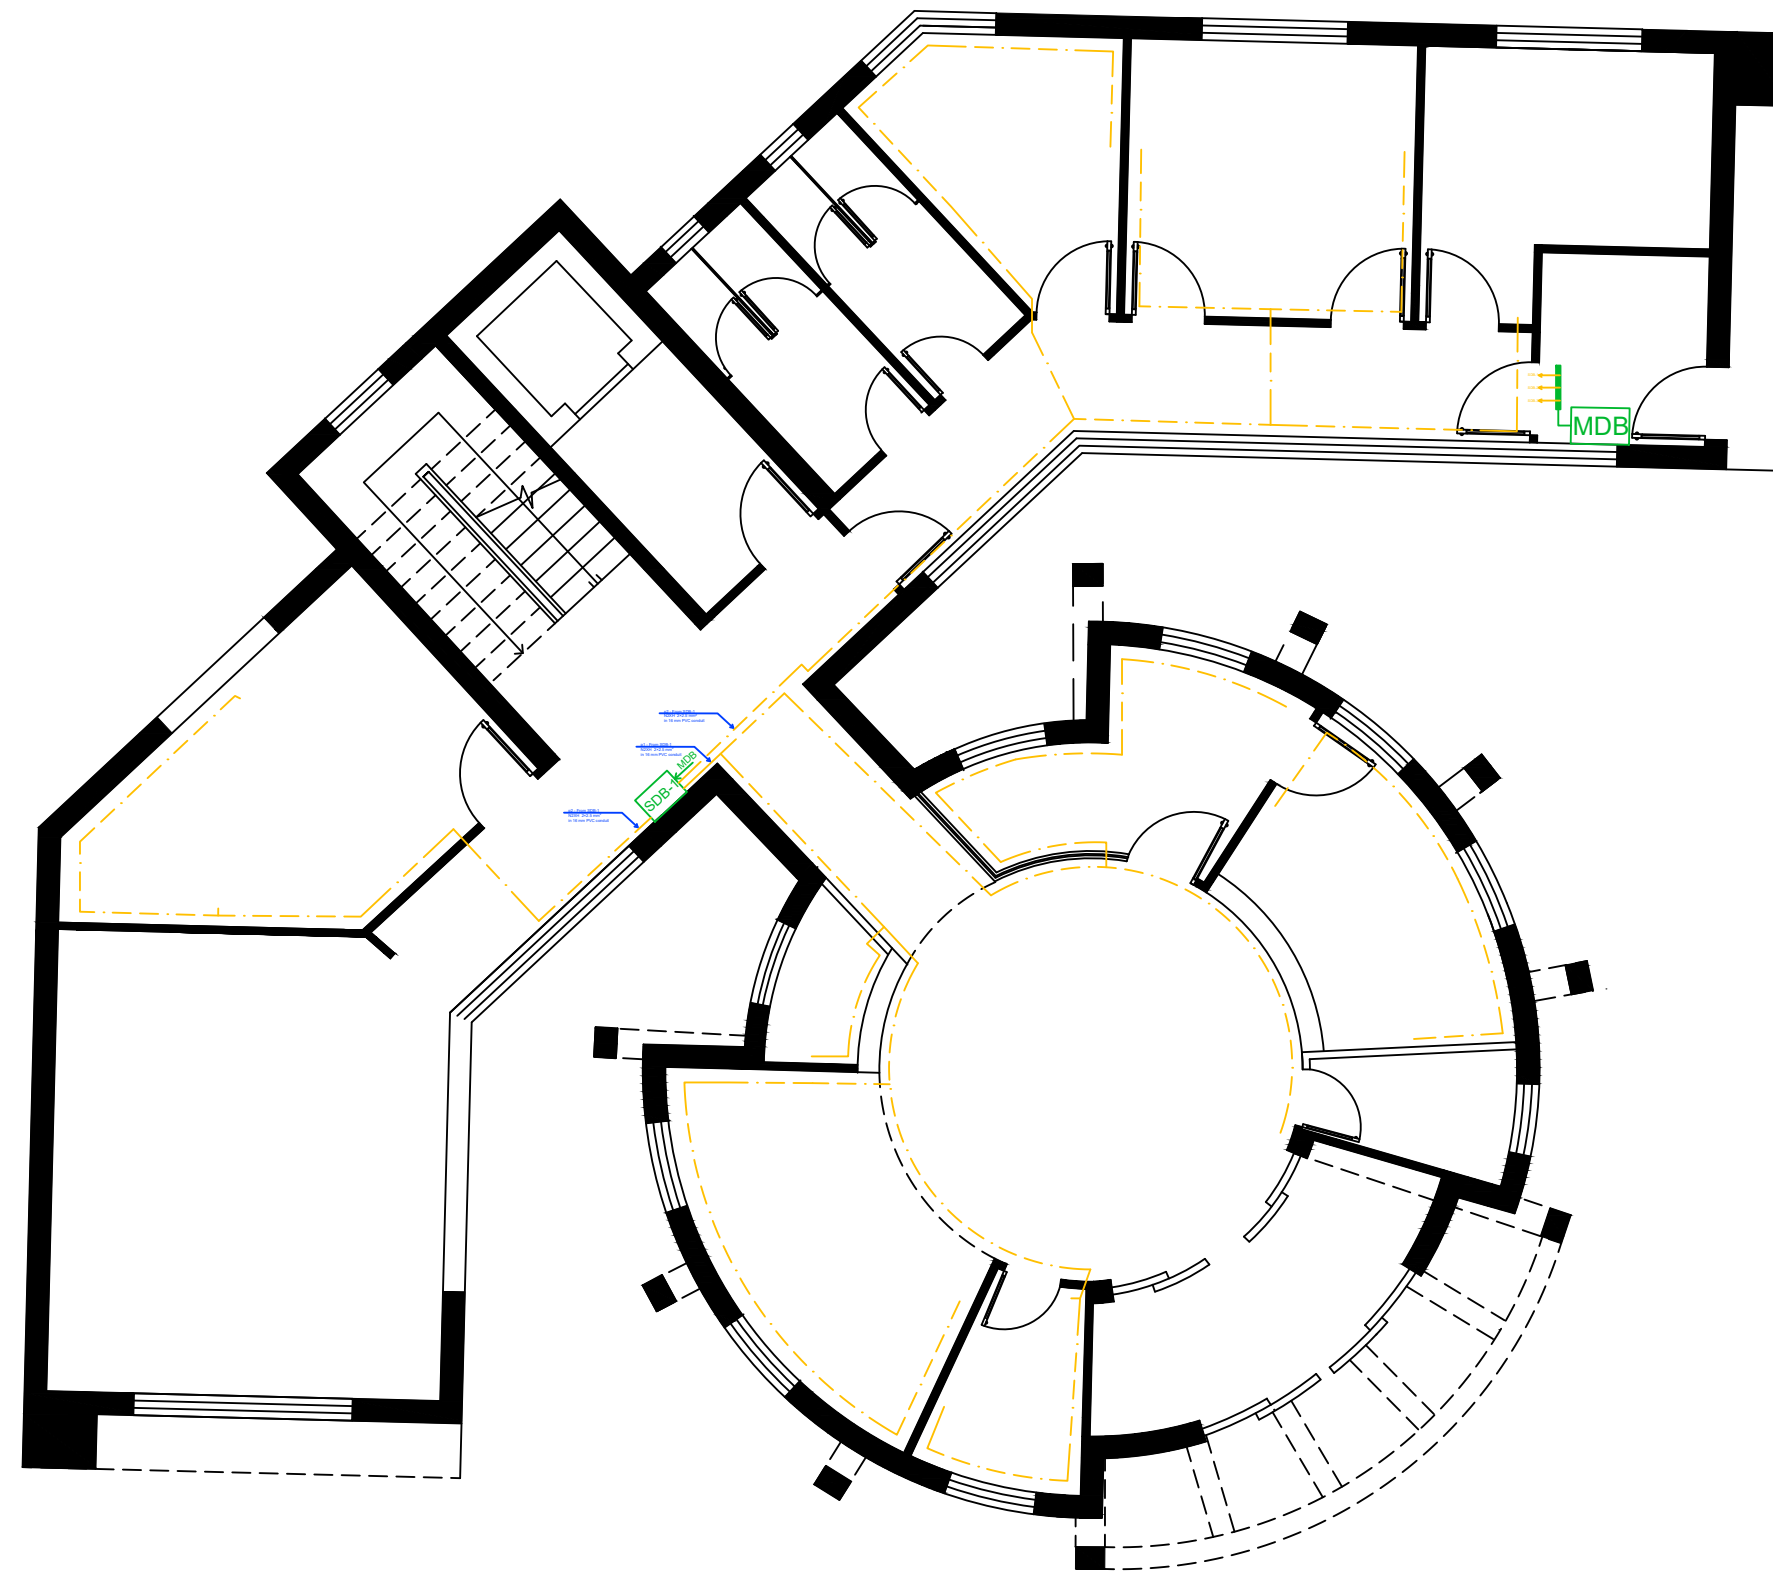

ground floor
scale 1:100